157

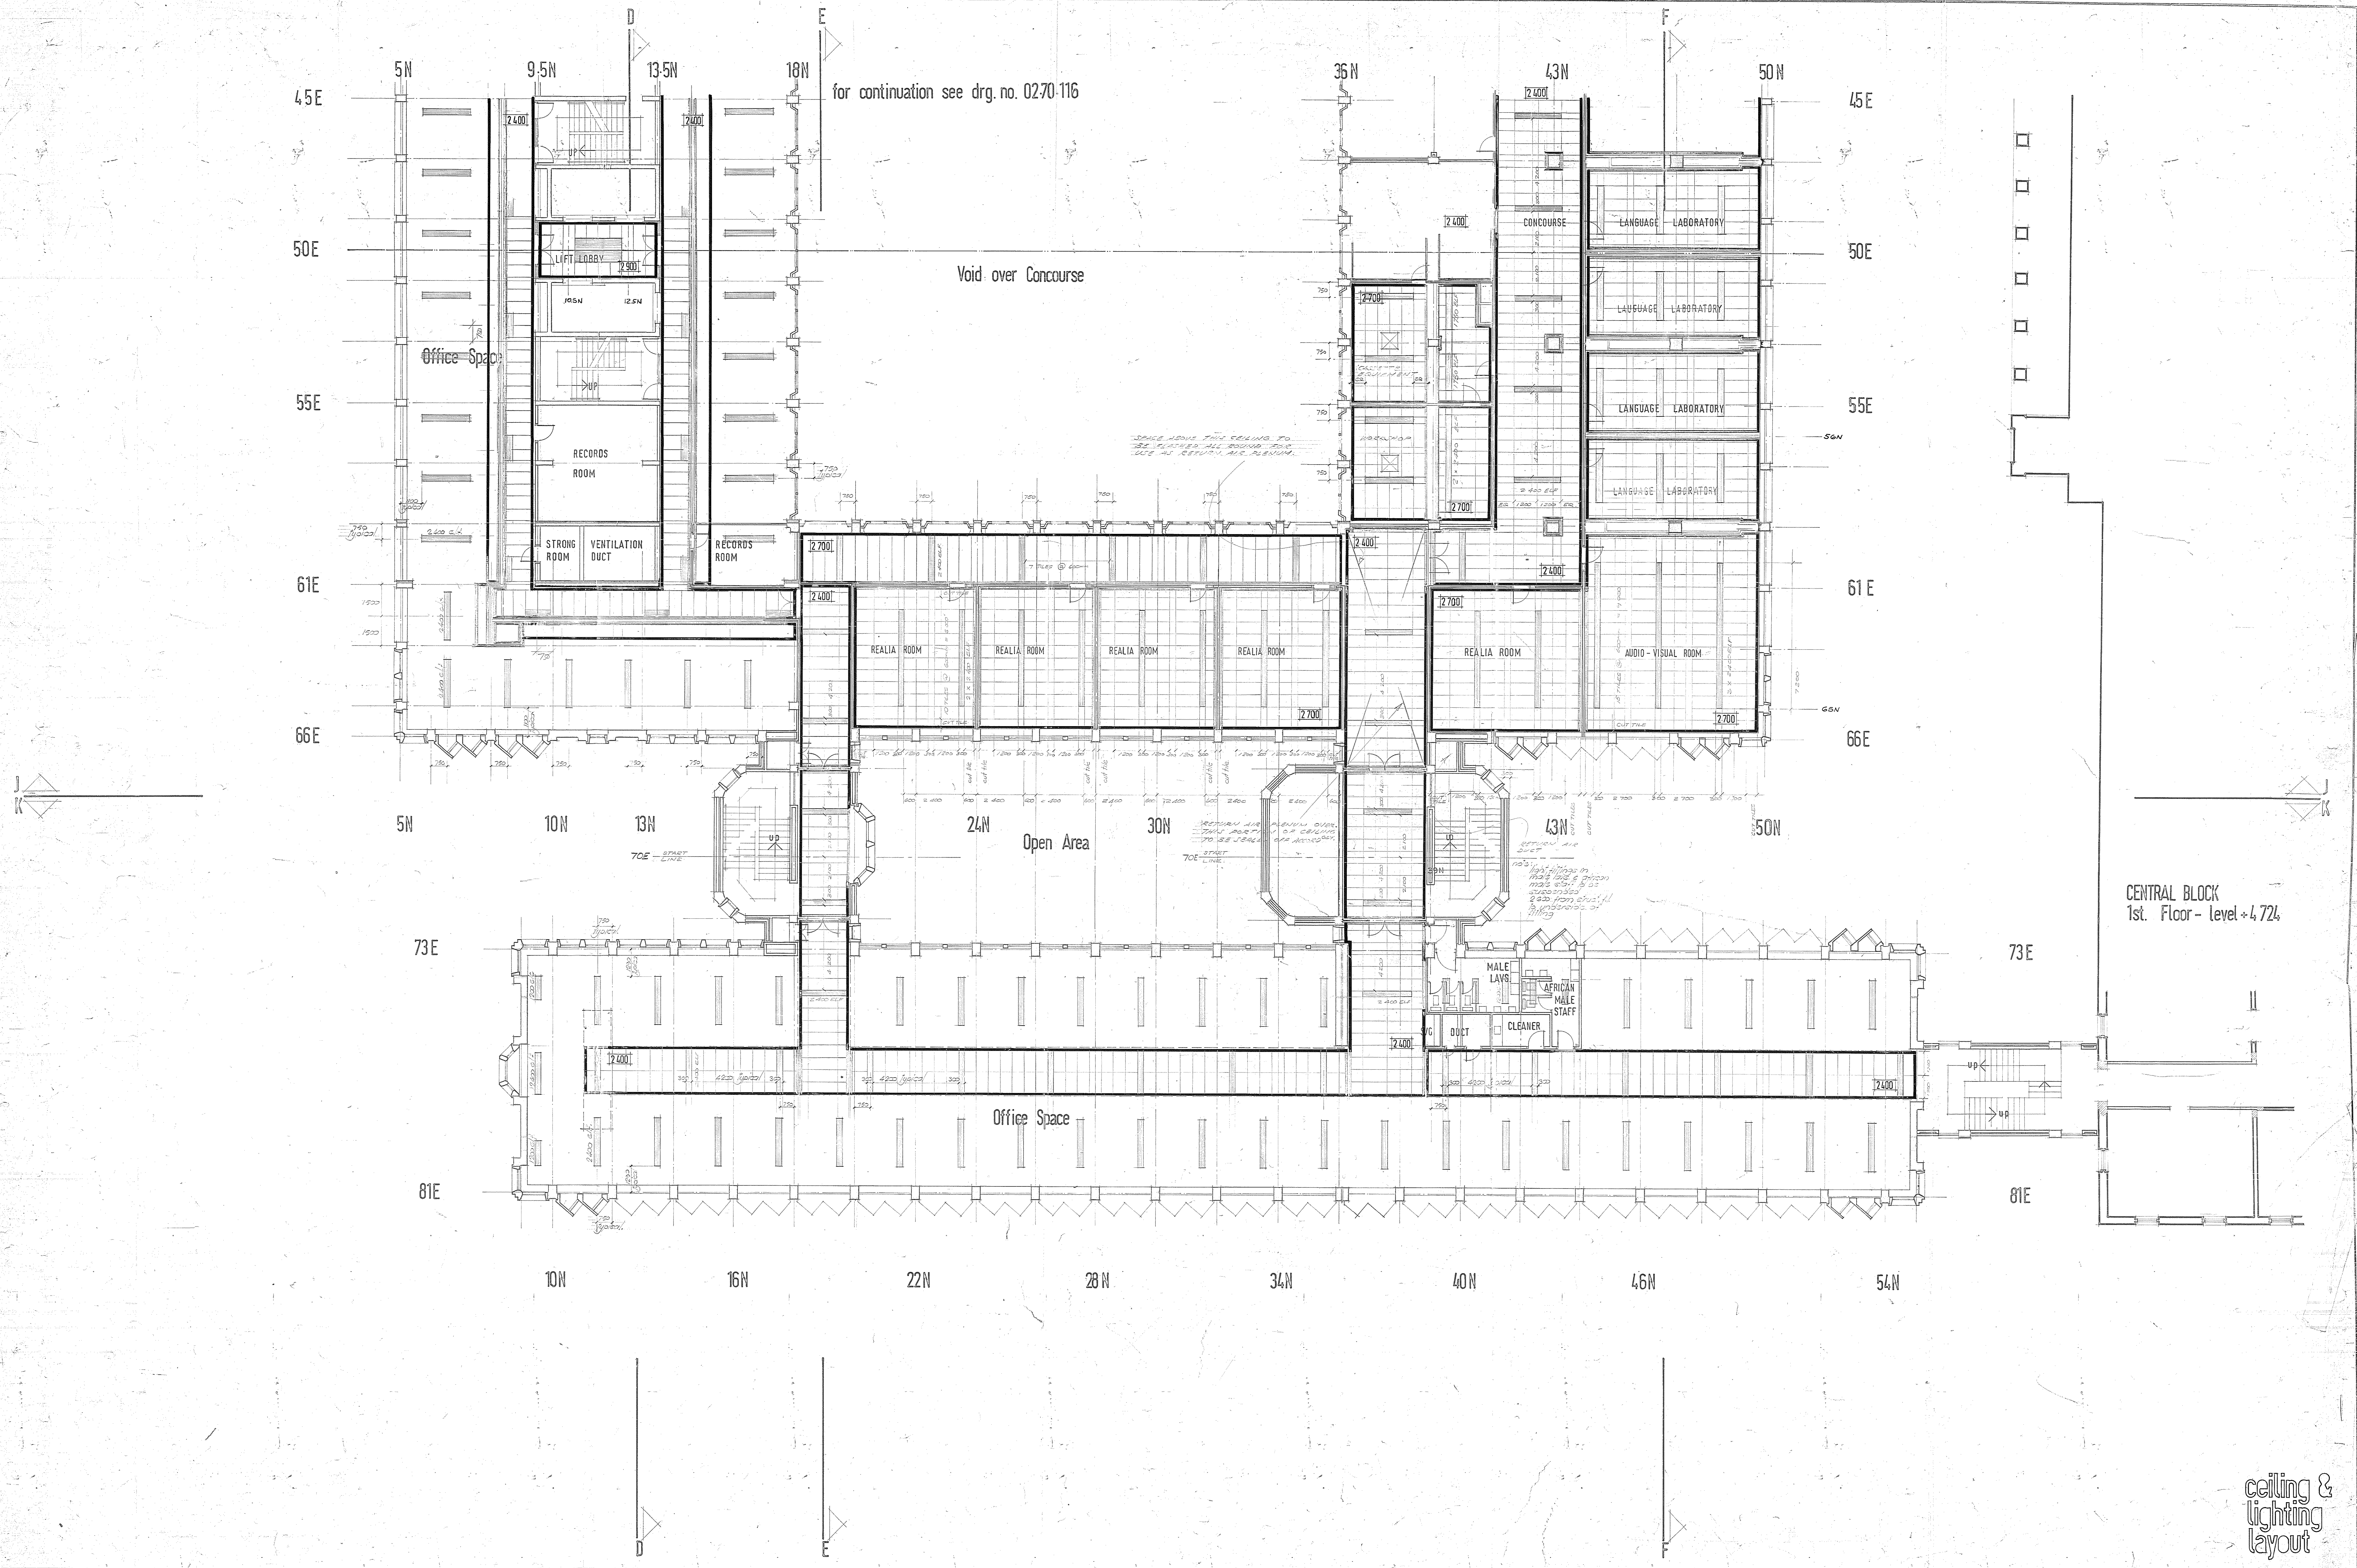

ceiling & lighting layout

all dimensions from underside of suspended ceilings to be taken from level +2 300
for all other lighting positions & information, refer to
electrical consultants drg. no. 145N.117.

No.	By	Date	REVISION
A	RWB	FEB 74	LANGUAGE LABORATORIES, WORKSHOP, REALIA ROOMS & CASSETTE EQUIPMENT MODIFIED
B	RWB	MAY 74	CEILING MODIFIED IN WAY OF DOOR AT 39N × 60E & RETURN AIR PLENUM NOTE ADDED
C	NO	FEB 75	TOWER BLOCK CEILINGS ALTERED

University of the Witwatersrand Johannesburg

MULTIPURPOSE BUILDING

PLAN AT LEVEL +6 900 East

JOHN FASSLER ASSOCIATES - ARCHITECTS
70 ST. ANDREWS ROAD, PARKTOWN
JOHANNESBURG. TEL. No. 44-9807/2

Scales ; 1 : 100
Drawn ; W.D/F.V
Date ; November 1971
Checked ;

Drawing Number
02.70.157

OZALID5986/9