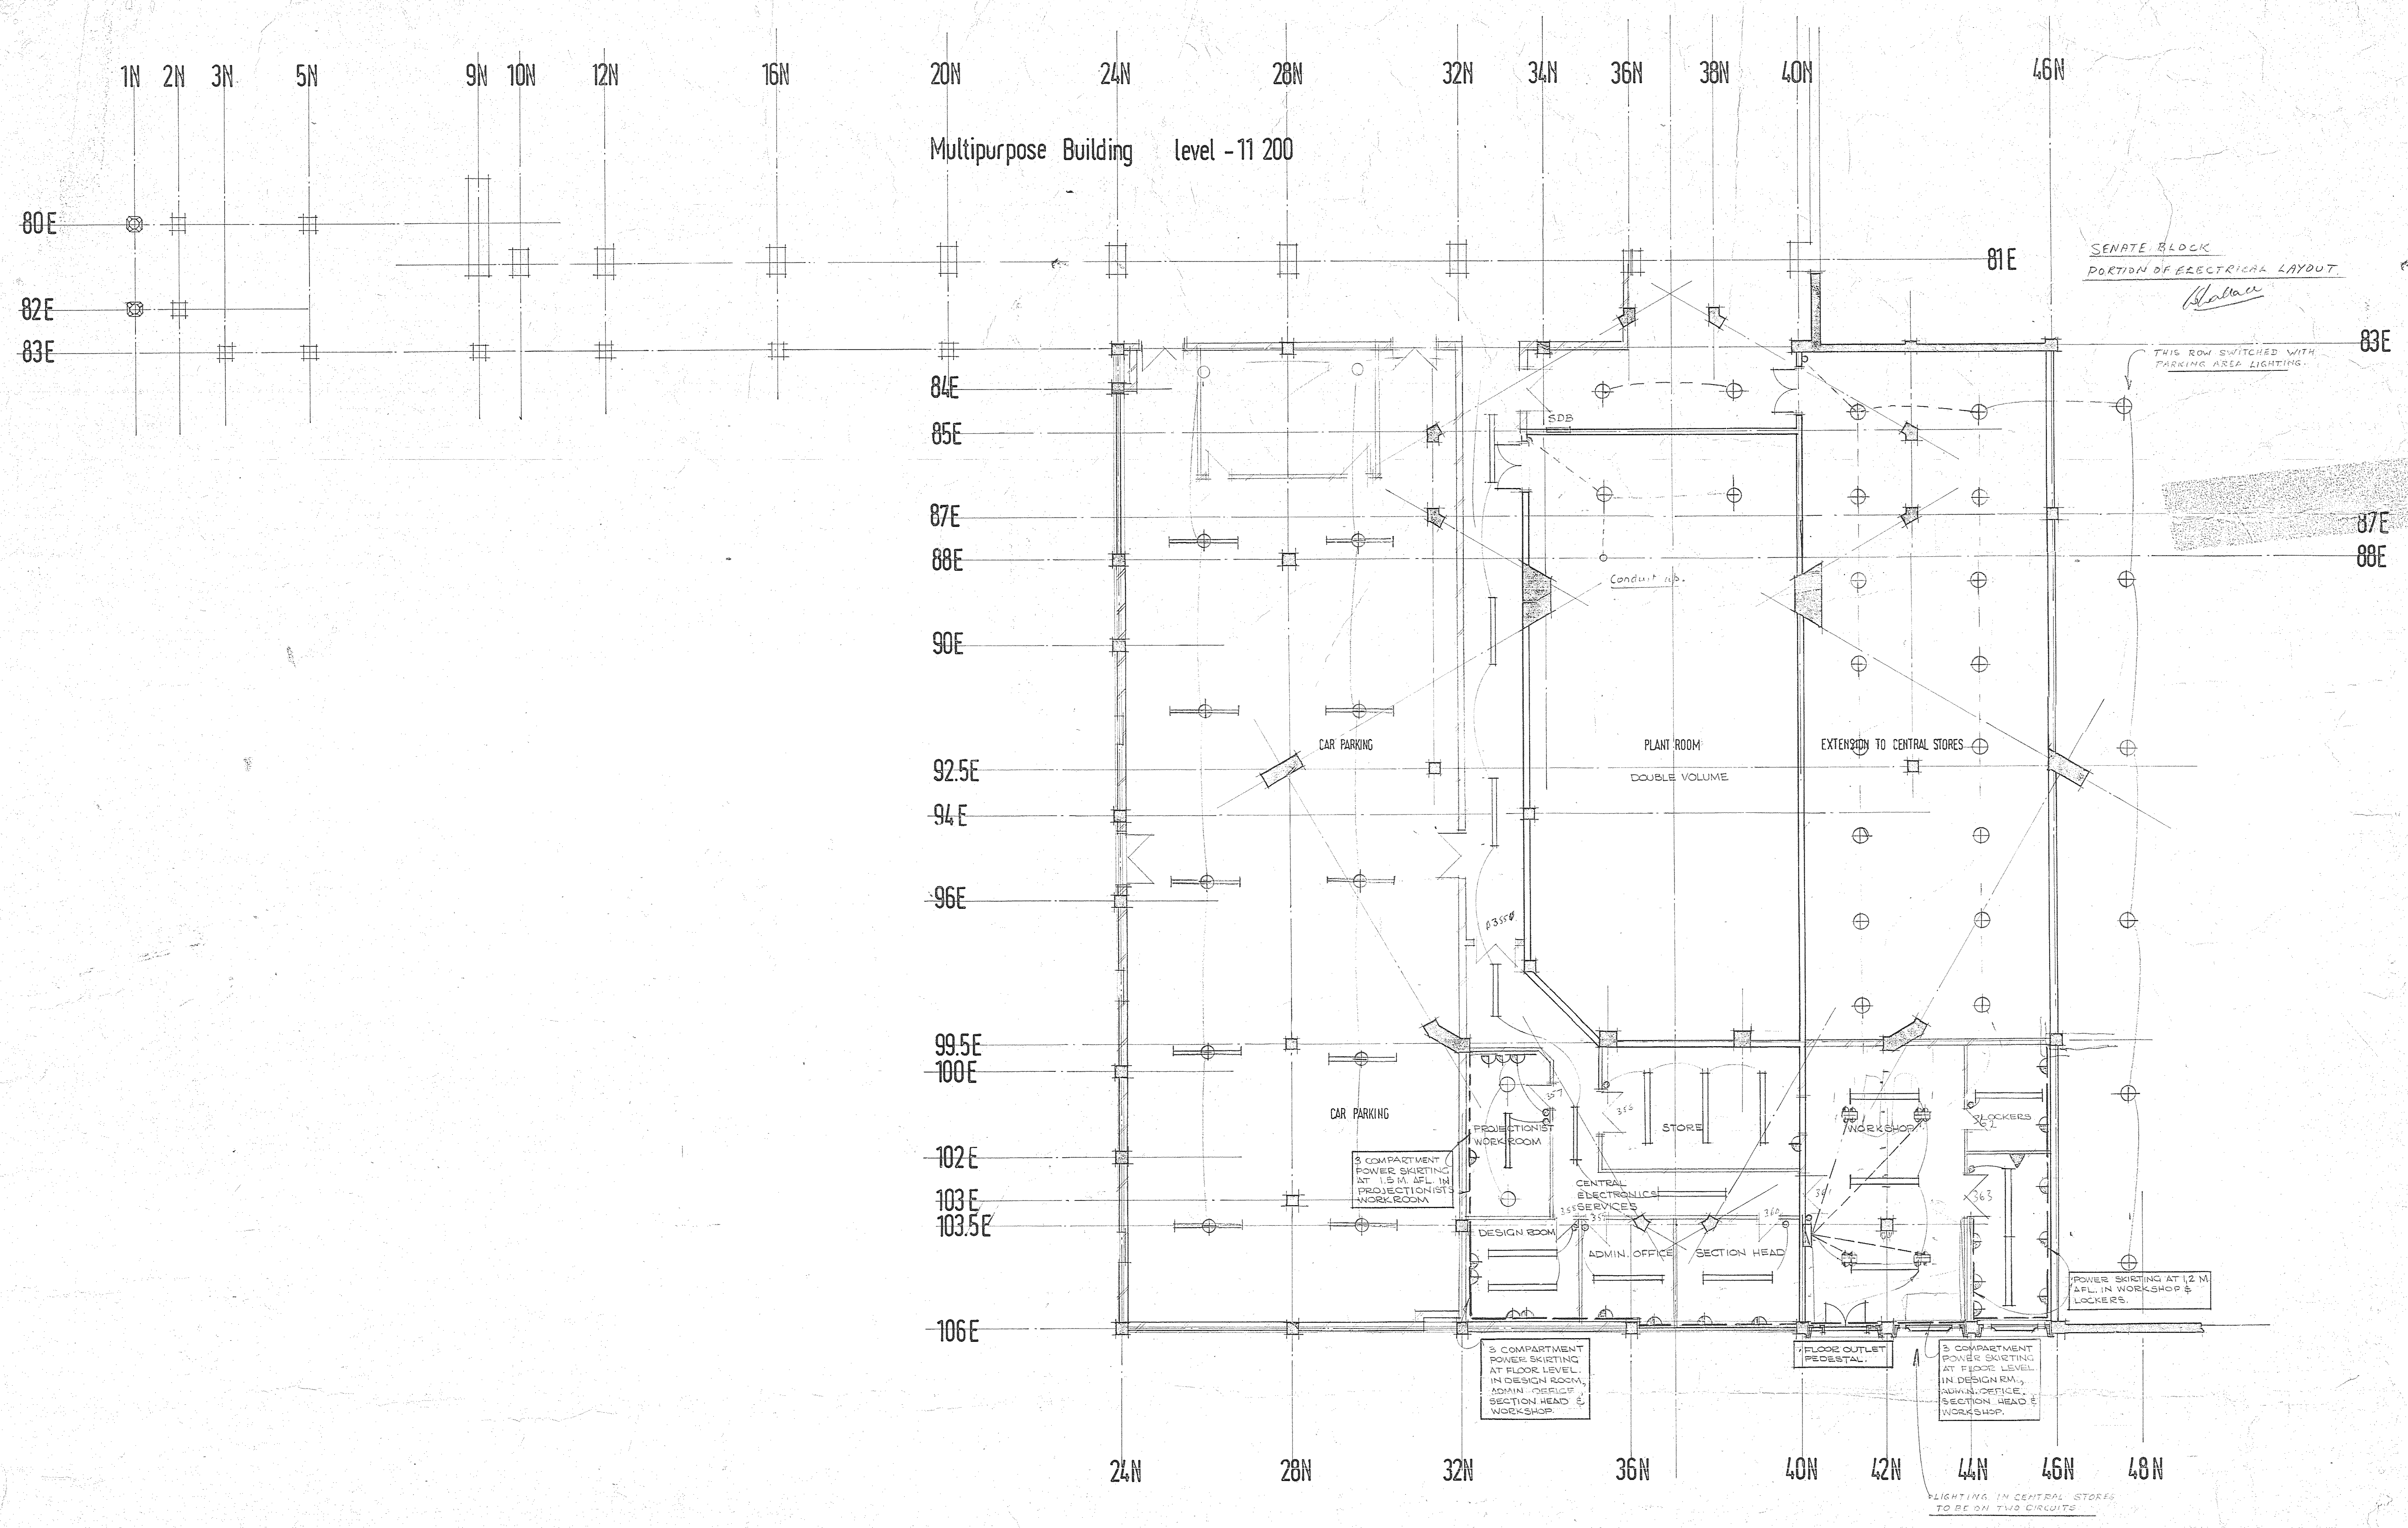
Multipurpose Building level -11 200
1N
2N
3N
5N
9N
10N
12N
16N
20N
24N
28N
32N
34N
36N
38N
40N
46N
80E
82E
83E
81E
84E
85E
87E
88E
90E
92.5E
94E
96E
99.5E
100E
102E
103E
103.5E
106E
SENATE BLOCK
PORTION OF ELECTRICAL LAYOUT
THIS ROW SWITCHED WITH PARKING AREA LIGHTING.
SDB
Conduit up.
CAR PARKING
PLANT ROOM
DOUBLE VOLUME
EXTENSION TO CENTRAL STORES
D355Ø
CAR PARKING
3 COMPARTMENT POWER SKIRTING AT 1.5 M. AFL. IN PROJECTIONISTS WORKROOM
PROJECTIONIST WORKROOM
357
356
STORE
CENTRAL ELECTRONICS SERVICES
355
359
DESIGN ROOM
ADMIN. OFFICE
SECTION HEAD
360
361
WORKSHOP
LOCKERS
362
363
POWER SKIRTING AT 1.2 M. AFL. IN WORKSHOP & LOCKERS.
3 COMPARTMENT POWER SKIRTING AT FLOOR LEVEL IN DESIGN ROOM, ADMIN. OFFICE SECTION HEAD & WORKSHOP.
FLOOR OUTLET PEDESTAL.
3 COMPARTMENT POWER SKIRTING AT FLOOR LEVEL IN DESIGN RM., ADMIN. OFFICE, SECTION HEAD & WORKSHOP.
24N
28N
32N
36N
40N
42N
44N
46N
48N
LIGHTING IN CENTRAL STORES TO BE ON TWO CIRCUITS

3 phase light in W/S area.
Each bench separate Ct.
Dimmer for Projectionist

Received 11-5-76

No.	By	Date	REVISION
			DWG NO. 145N1011 LEVEL 11-200 ELECTRICAL INSTALLATIONS

University of the Wi srand Johannes

MULTIPURPOSE BUILDI