Plan at deck level

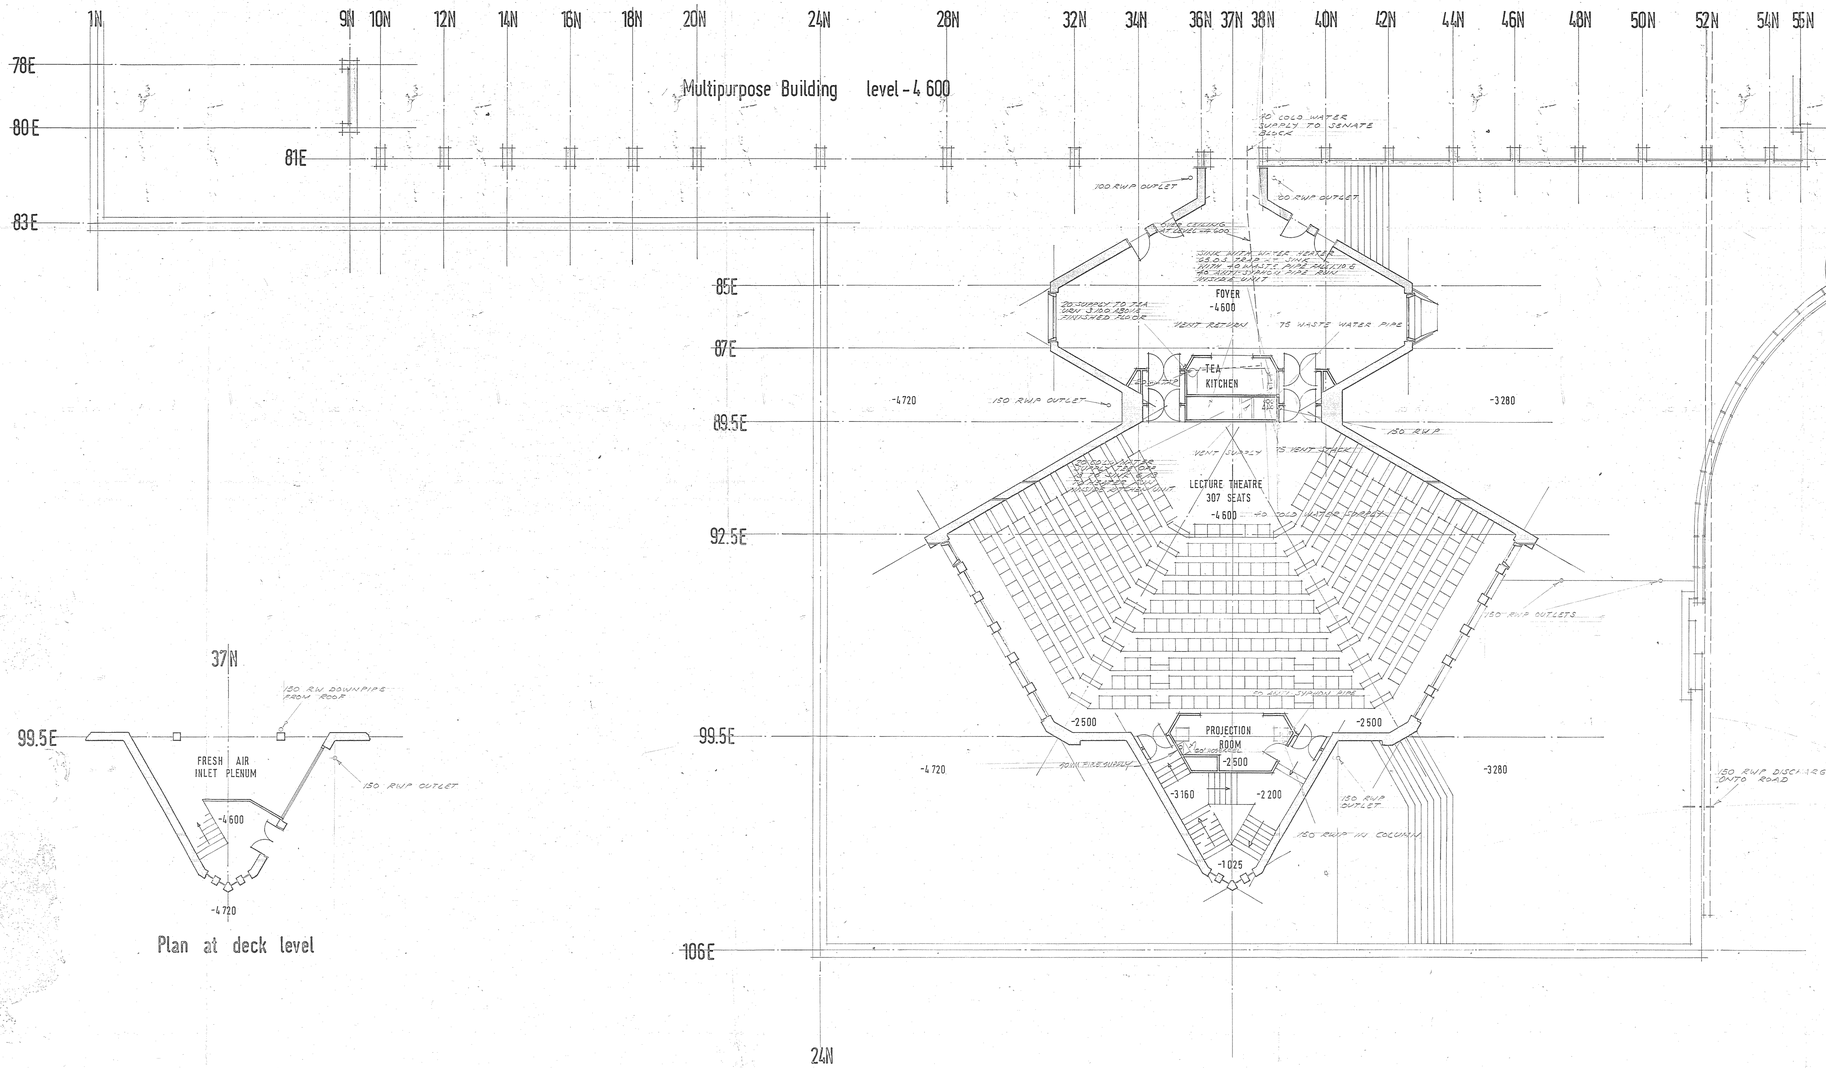

Water Reticulation & Drainage

No.	By	Date	REVISION

University of the Witwatersrand Johannesburg

MULTIPURPOSE BUILDING

SENATE BLOCK Plan at level -4 600

JOHN FASSLER ASSOCIATES - ARCHITECTS
10 ST. ANDREWS ROAD, PARKTOWN
JOHANNESBURG. TEL. No. 44-9361/2

Scales : 1:100
Drawn : WD/RVE
Date : Jan 75
Checked:

Drawing Number 02-701023

Water Reticulation/Drainage/1023