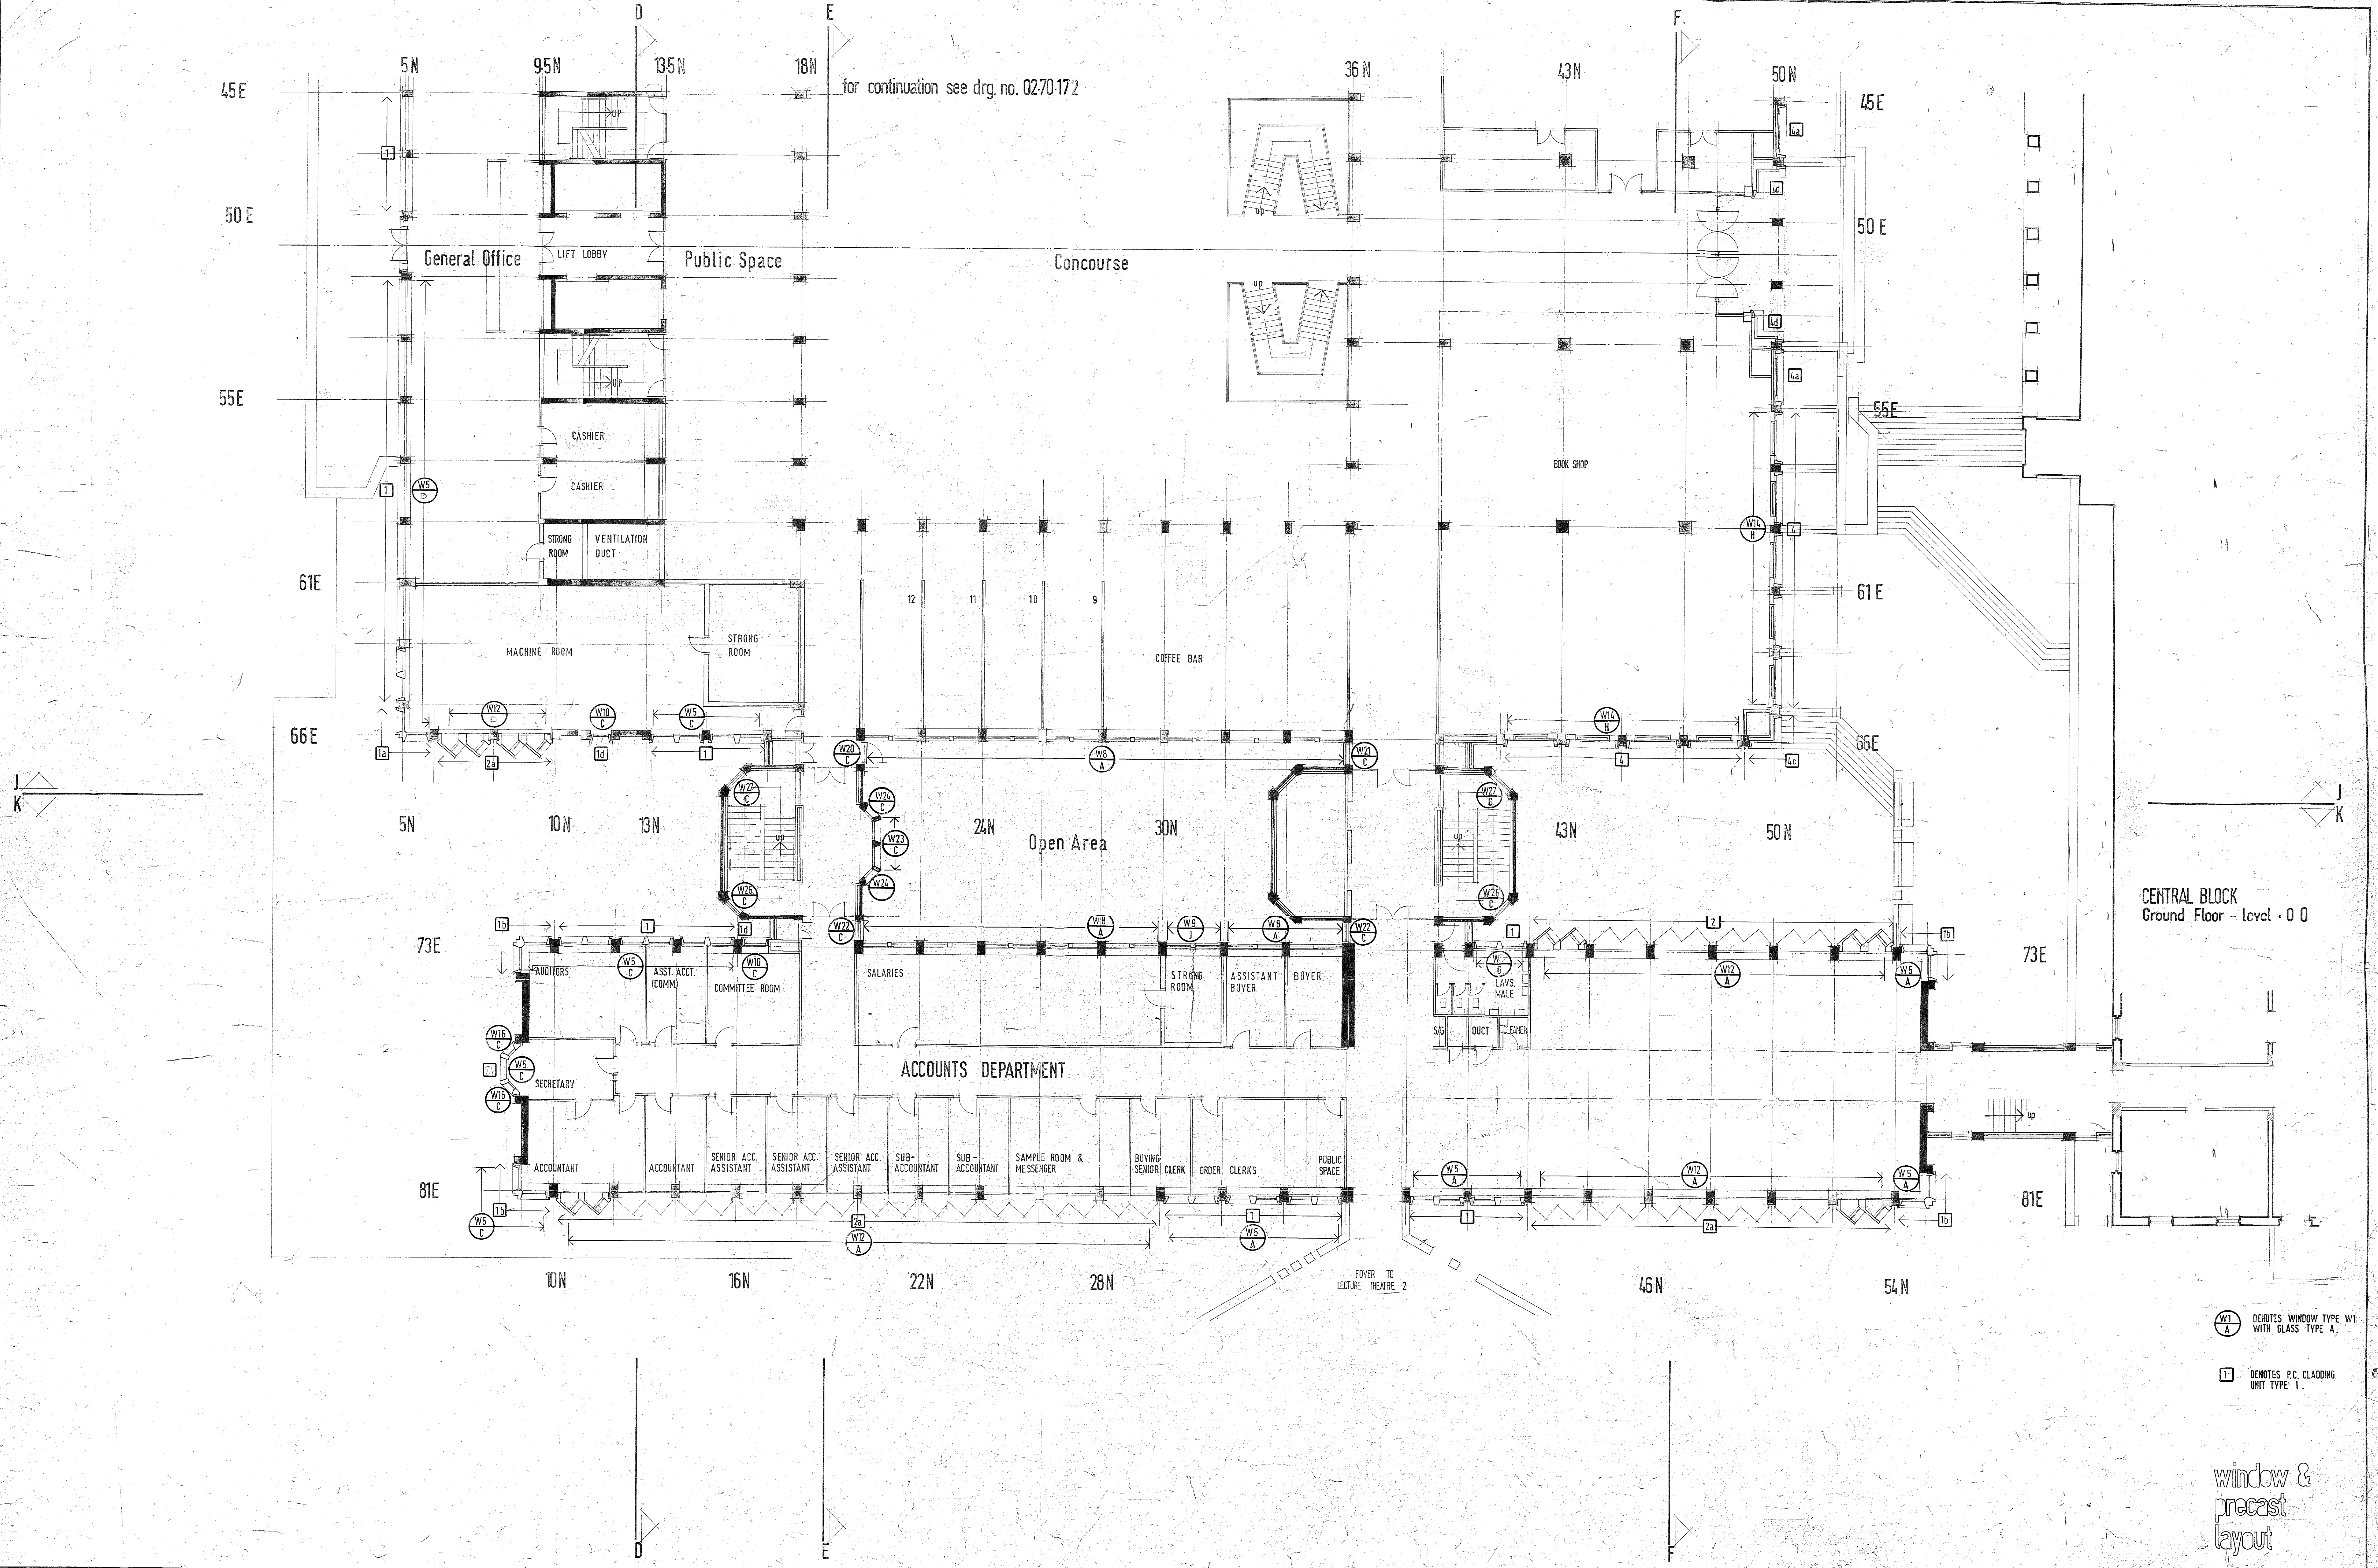

W1 / A DENOTES WINDOW TYPE W1 WITH GLASS TYPE A.

1 DENOTES P.C. CLADDING UNIT TYPE 1.

window & precast layout

No.	By	Date	REVISION
A	W.D	[illegible]	TYPE 7 ALTERTED TO TYPE 7A CLADDING.
B	W.D	5.72	WINDOW TYPE 7 ALTERED TO TYPE 5
C	MS	[illegible]	Cladding to South façade & portion of East façade Tower Block altered

University of the Witwatersrand Johannesburg

MULTIPURPOSE BUILDING

PLAN AT LEVEL + 0 0 East

JOHN FASSLER ASSOCIATES – ARCHITECTS
10 ST. ANDREWS ROAD, PARKTOWN
JOHANNESBURG. TEL. No. 44-0361/2

Scales ; 1 : 100
Drawn ; W.D / F.V.
Date ; November 1971
Checked ;

Drawing Number
02·70·173

OZALID b986/9.