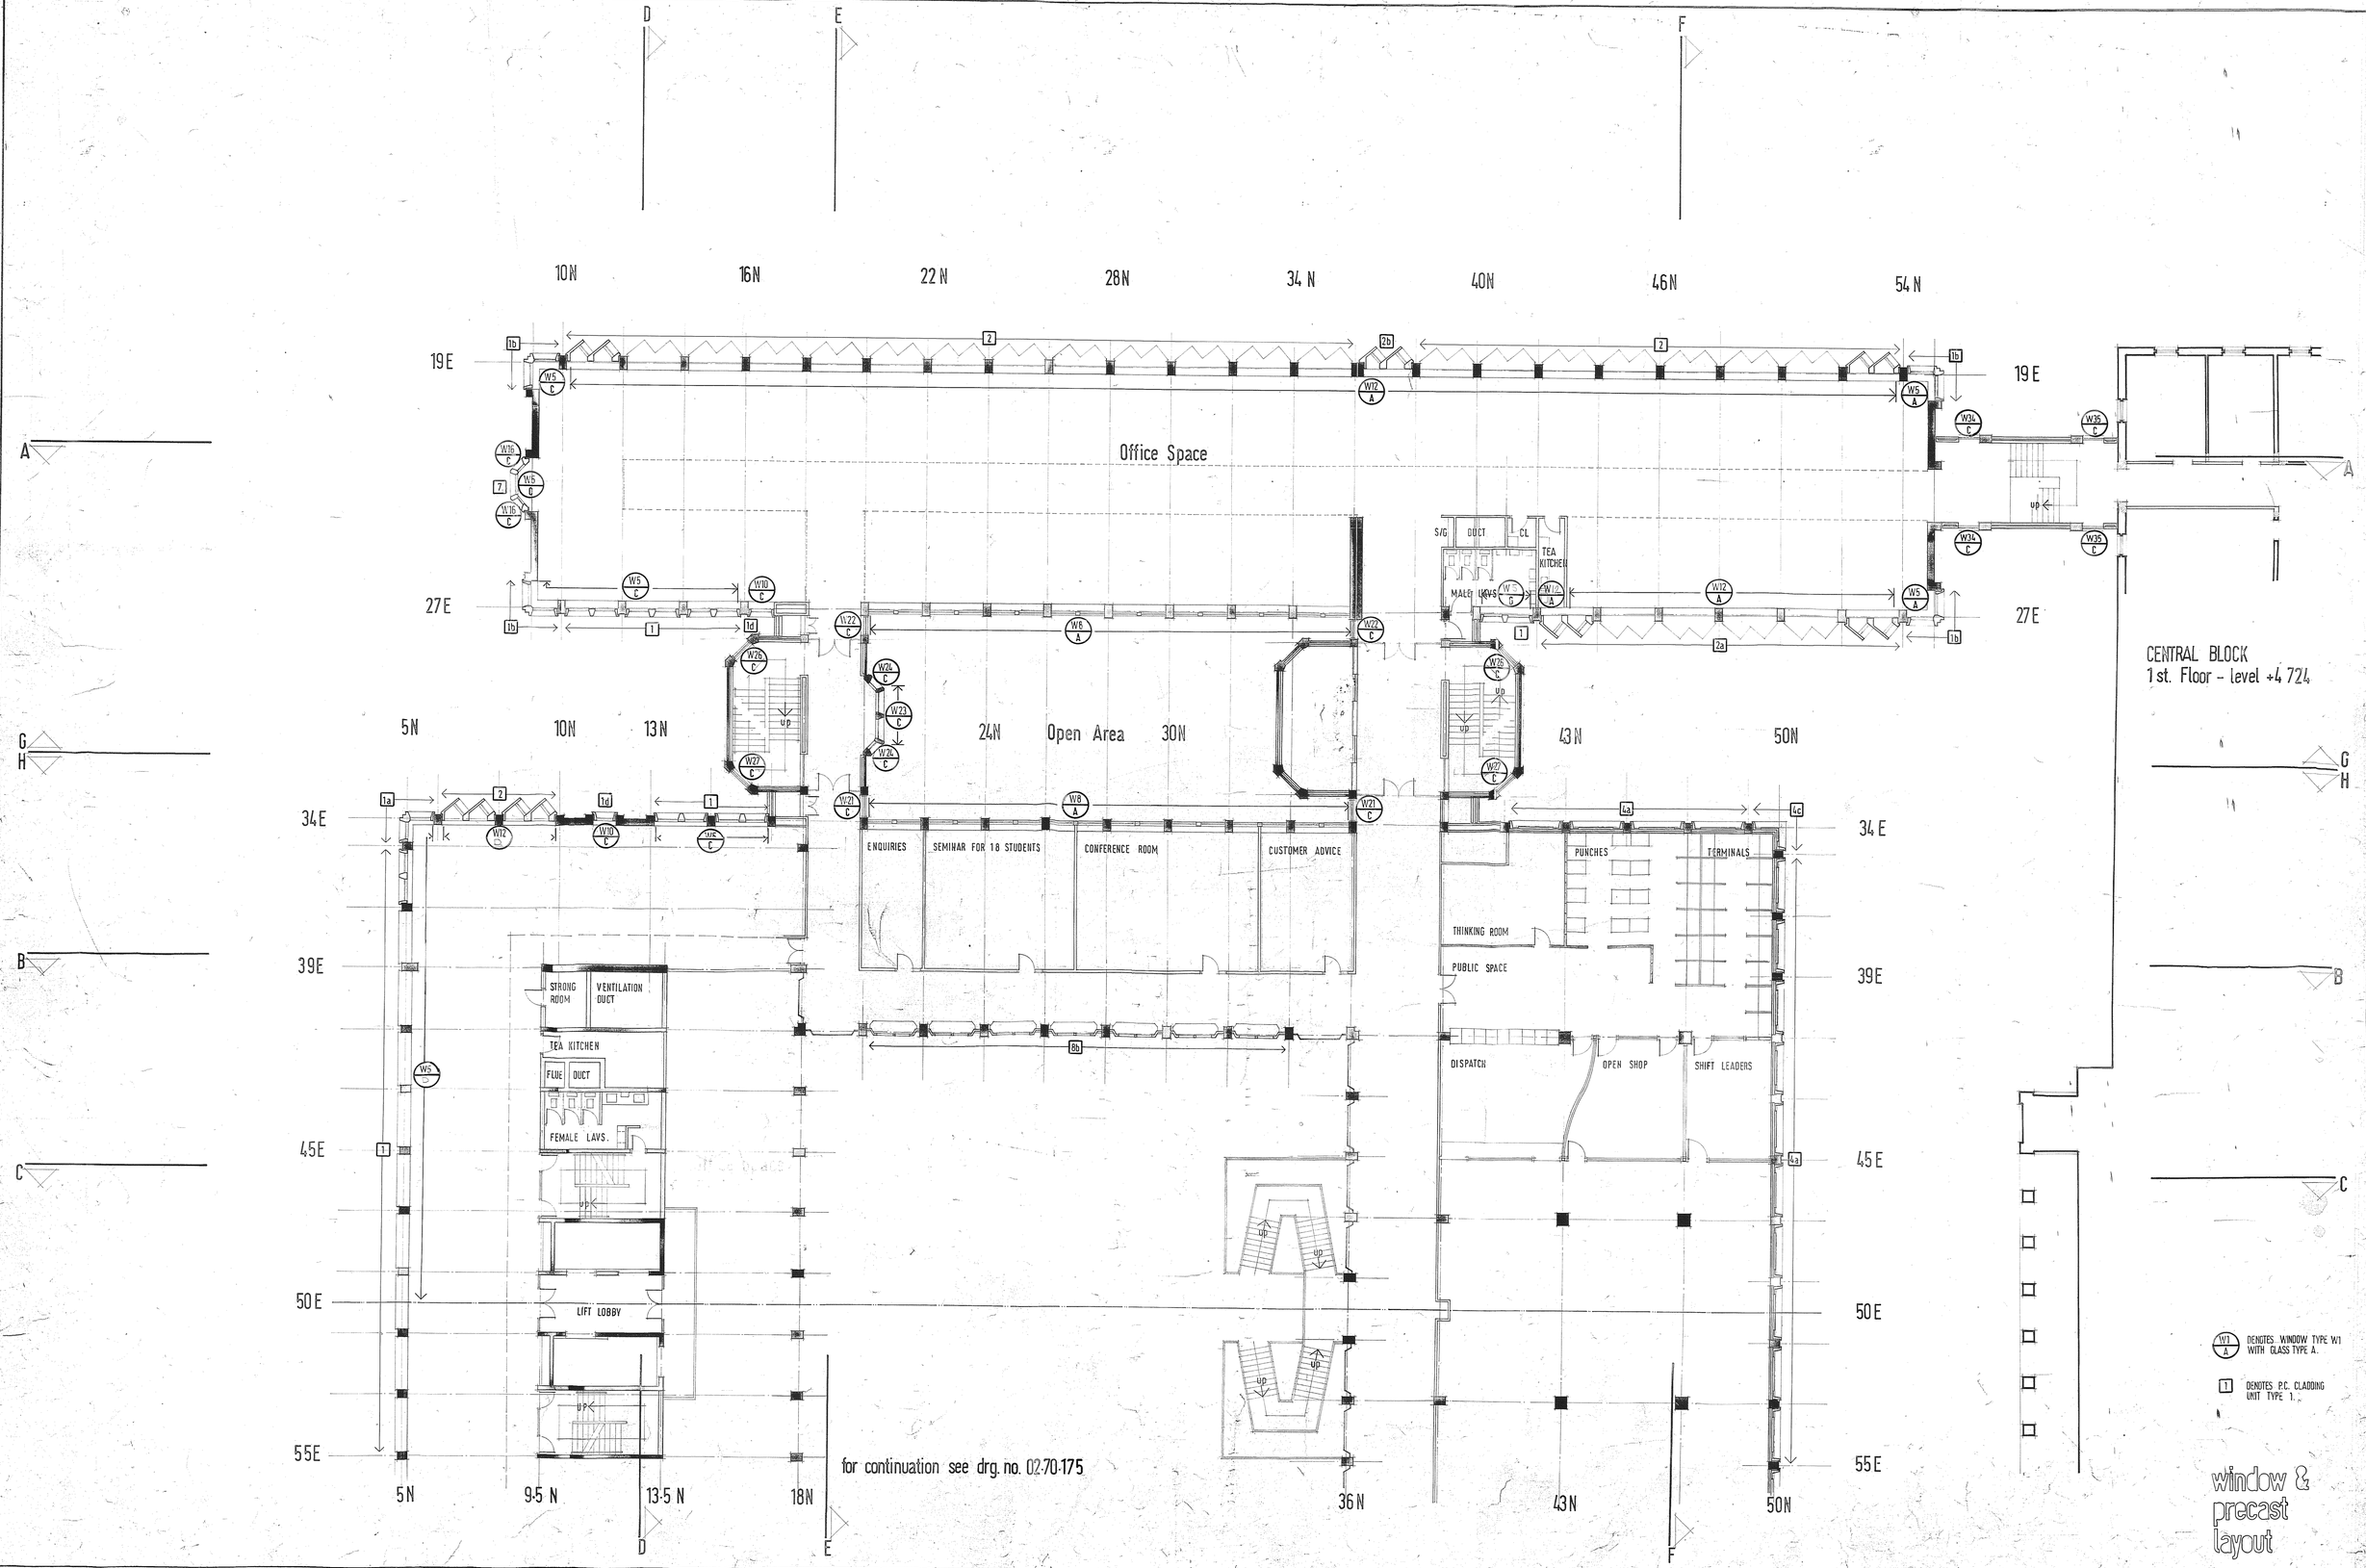


| No. | By | Date | REVISION |
|---|---|---|---|
| | | MAY'71 | WINDOW TYPE 7 REPLACED IN TYPE 5 AND TYPE 15 THROUGHOUT |

University of the Witwatersrand Johannesburg

# MULTIPURPOSE BUILDING

## PLAN AT LEVEL +3 450 West

JOHN FASSLER ASSOCIATES - ARCHITECTS
10 ST. ANDREWS ROAD, PARKTOWN
JOHANNESBURG. TEL. No. 44-8361/2

Scales 1 : 100
Drawn : W.D/F.V
Date : November 1971
Checked :

Drawing Number 02-70-174

OZALID/SSS/6.