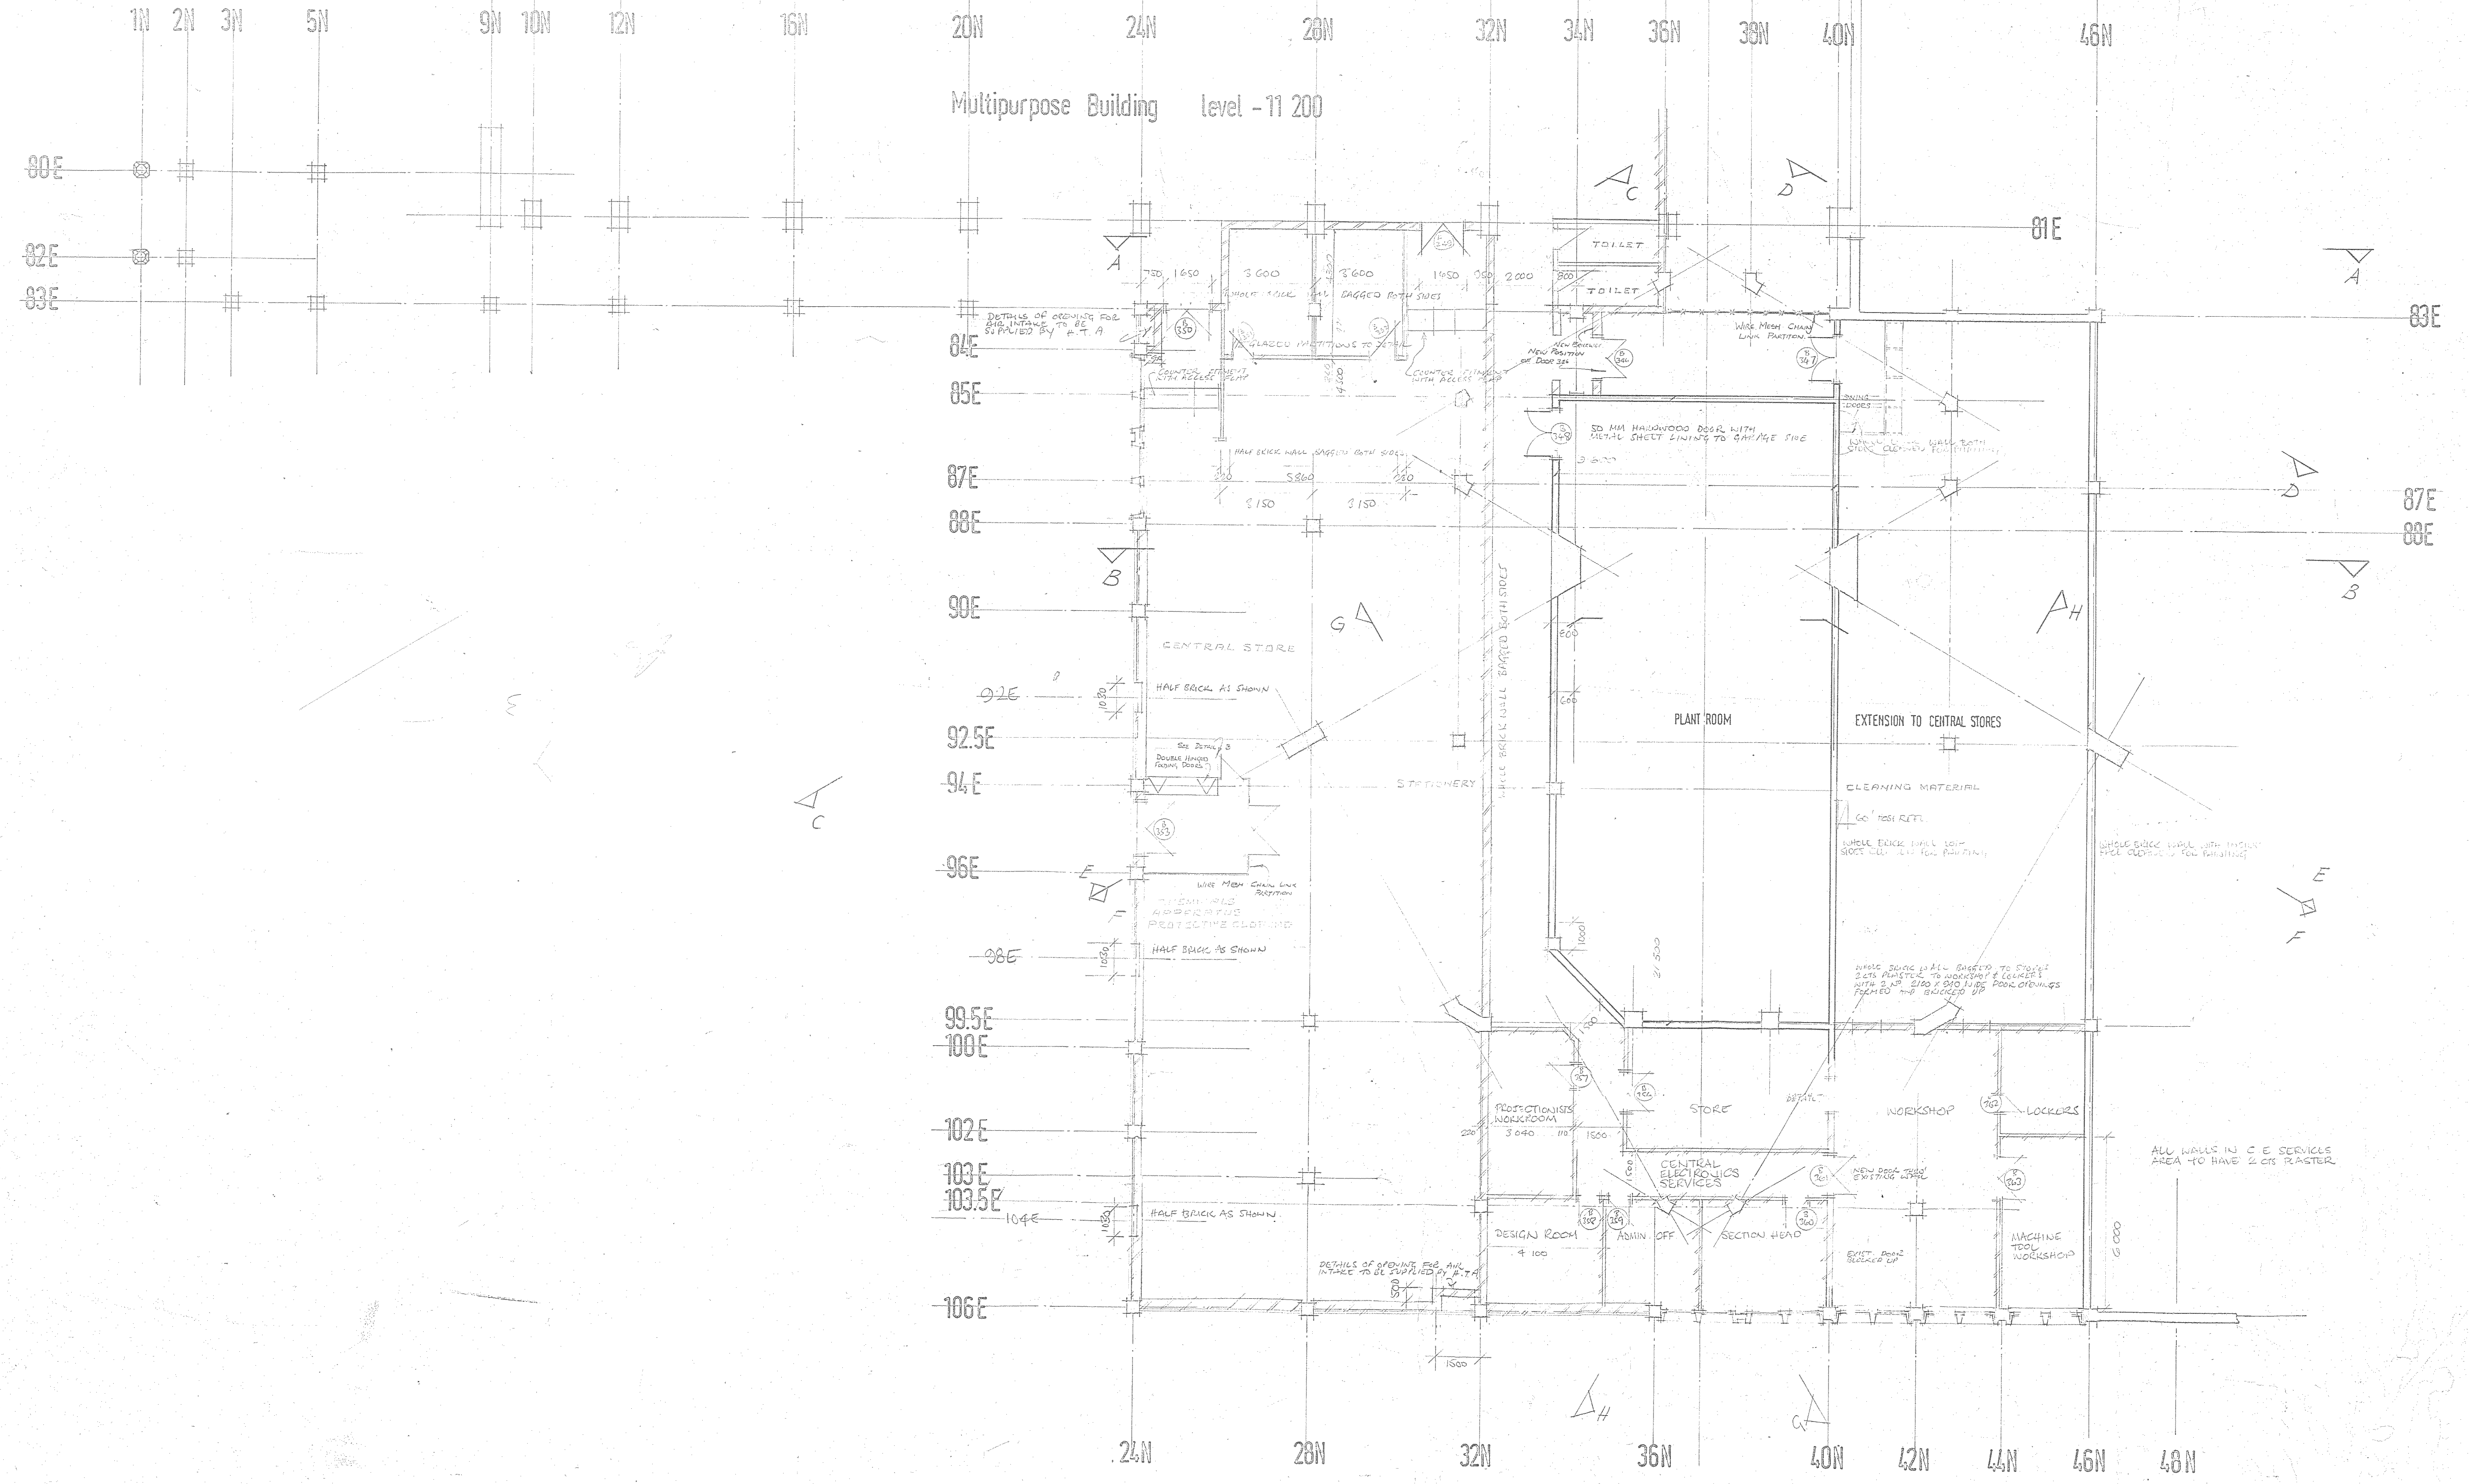
Multipurpose Building level -11 200
1N 2N 3N 5N 9N 10N 12N 16N 20N 24N 28N 32N 34N 36N 38N 40N 46N
80E
82E
83E
84E
85E
87E
88E
90E
91E
92.5E
94E
96E
98E
99.5E
100E
102E
103E
103.5E
104E
106E
81E
A
B
C
D
E
F
G
H
TOILET
TOILET
750 1650 3600 3600 1450 050 2000 800
WHOLE BRICK
BAGGED BOTH SIDES
DETAILS OF OPENING FOR AIR INTAKE TO BE SUPPLIED BY H.T.A
GLAZED PARTITIONS TO DETAIL
COUNTER FITMENT WITH ACCESS FLAP
COUNTER FITMENT WITH ACCESS FLAP
NEW BRICKWORK
NEW POSITION OF DOOR 346
WIRE MESH CHAIN LINK PARTITION.
SWING DOORS
50 MM HARDWOOD DOOR WITH METAL SHEET LINING TO GARAGE SIDE
WHOLE BRICK WALL BOTH SIDES CLEANED FOR PAINTING
HALF BRICK WALL BAGGED BOTH SIDES
220 5860 220
3150 3150
WHOLE BRICK WALL BAGGED BOTH SIDES
CENTRAL STORE
HALF BRICK AS SHOWN
1030
SEE DETAIL B
DOUBLE HINGED FOLDING DOORS
STATIONERY
PLANT ROOM
EXTENSION TO CENTRAL STORES
CLEANING MATERIAL
60' HOSE REEL
WHOLE BRICK WALL BOTH SIDES CLEANED FOR PAINTING
WHOLE BRICK WALL WITH INSIDE FACE CLEANED FOR PAINTING
WIRE MESH CHAIN LINK PARTITION
CHEMICALS
APPARATUS
PROTECTIVE CLOTHING
HALF BRICK AS SHOWN
800 600 1000 21 500
WHOLE BRICK WALL BAGGED TO STORES 2 CTS PLASTER TO WORKSHOP & LOCKERS WITH 2 No 2100 X 940 WIDE DOOR OPENINGS FORMED AND BRICKED UP
PROJECTIONISTS WORKROOM
220 3040 110 1500
STORE
DETAIL
WORKSHOP
LOCKERS
CENTRAL ELECTRONICS SERVICES
1500
NEW DOOR THRO' EXISTING WALL
DESIGN ROOM
4 100
ADMIN. OFF
SECTION HEAD
EXIST. DOOR BLOCKED UP
MACHINE TOOL WORKSHOP
6 000
ALL WALLS IN C.E. SERVICES AREA TO HAVE 2 CTS PLASTER
HALF BRICK AS SHOWN
DETAILS OF OPENING FOR AIR INTAKE TO BE SUPPLIED BY H.T.A
500
1500
B 346
B 347
B 348
B 349
B 350
B 351
B 352
B 353
B 356
B 357
B 358
B 359
B 360
B 361
362
B 363
24N 28N 32N 36N 40N 42N 44N 46N 48N

CAR PARKING AREA NATURALLY CROSS VENTILATED
CENTRAL STORES MECHANICALLY VENTILATED MINIMUM 8 CHANGES/HOUR

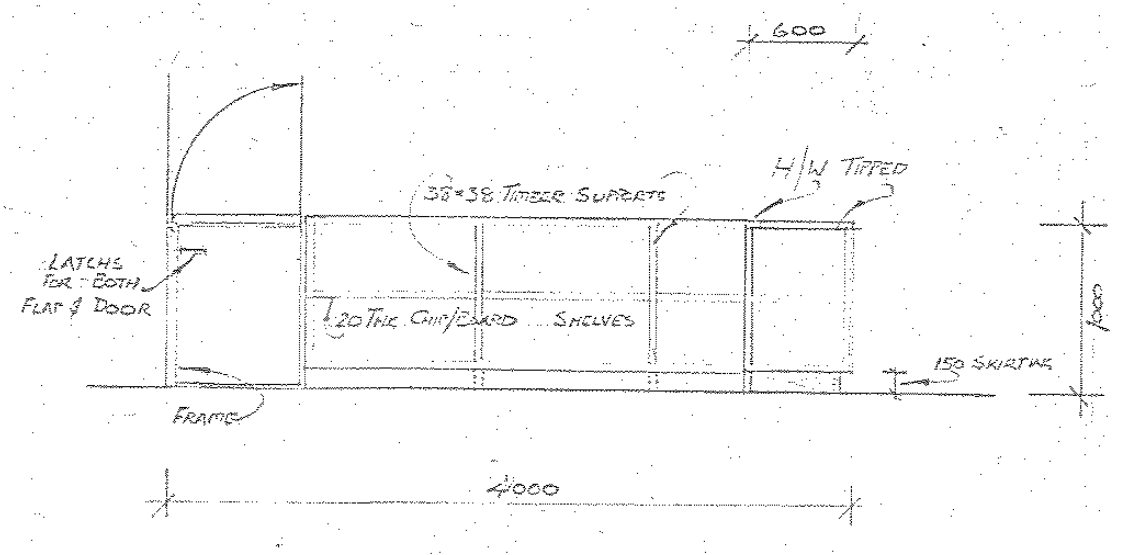

ELEVATION OF COUNTER. DETAIL 'A'
SCALE 1:50

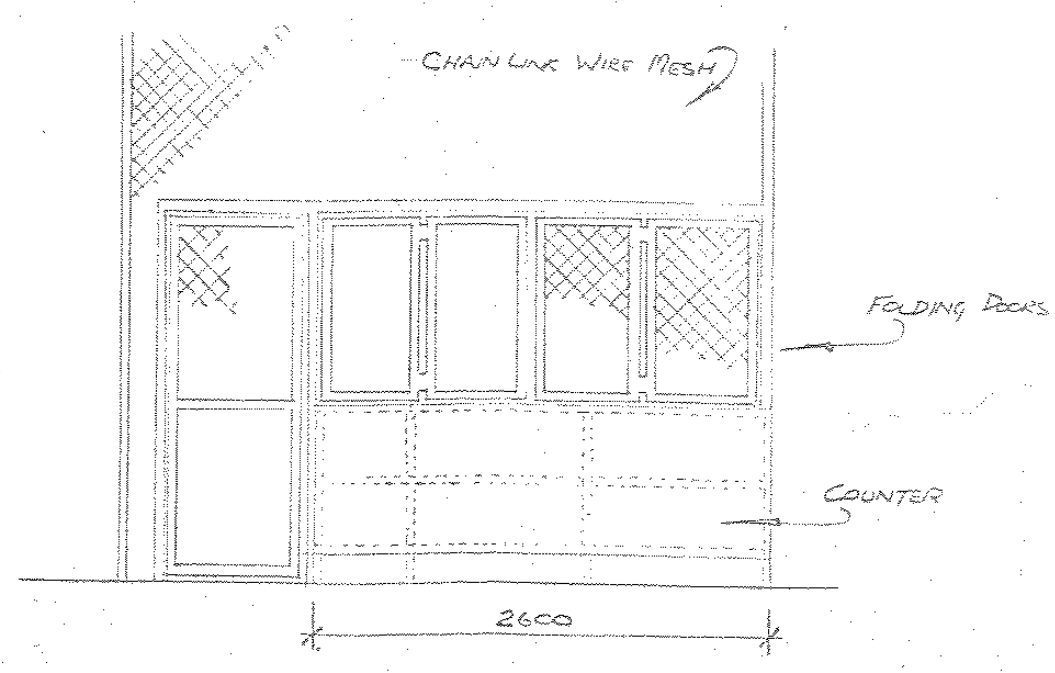

ELEVATION OF SLIDING DOORS. DETAIL 'B'
SCALE 1:50

PLANT AT LEVEL -11 20

B3 02-70-10

No.	By	Date	REVISION
A	WD	2.76	CENTRAL STORES & CENTRAL ELECTRONICS SERVICES ADDED
B	WD	3.76	DOOR NUMBERS ADDED
C	PS	5.76	NEW PARTITIONS, COUNTERS & DOOR (366) REPLACED
D	[illegible]	[illegible]	SERVERY COUNTER

University of the Witwatersrand Johannesburg

MULTIPURPOSE BUILDING

SENATE BLOCK

JOHN FASSLER ASSOCIATES - ARCHITECTS
10 ST. ANDREWS ROAD, PARKTOWN
JOHANNESBURG. TEL. No. 44-6391/2

Plan at level -11

Scales : 1:100
Drawn : W.D.
Date : JAN 1973
Checked :

Drawing Number
02-70