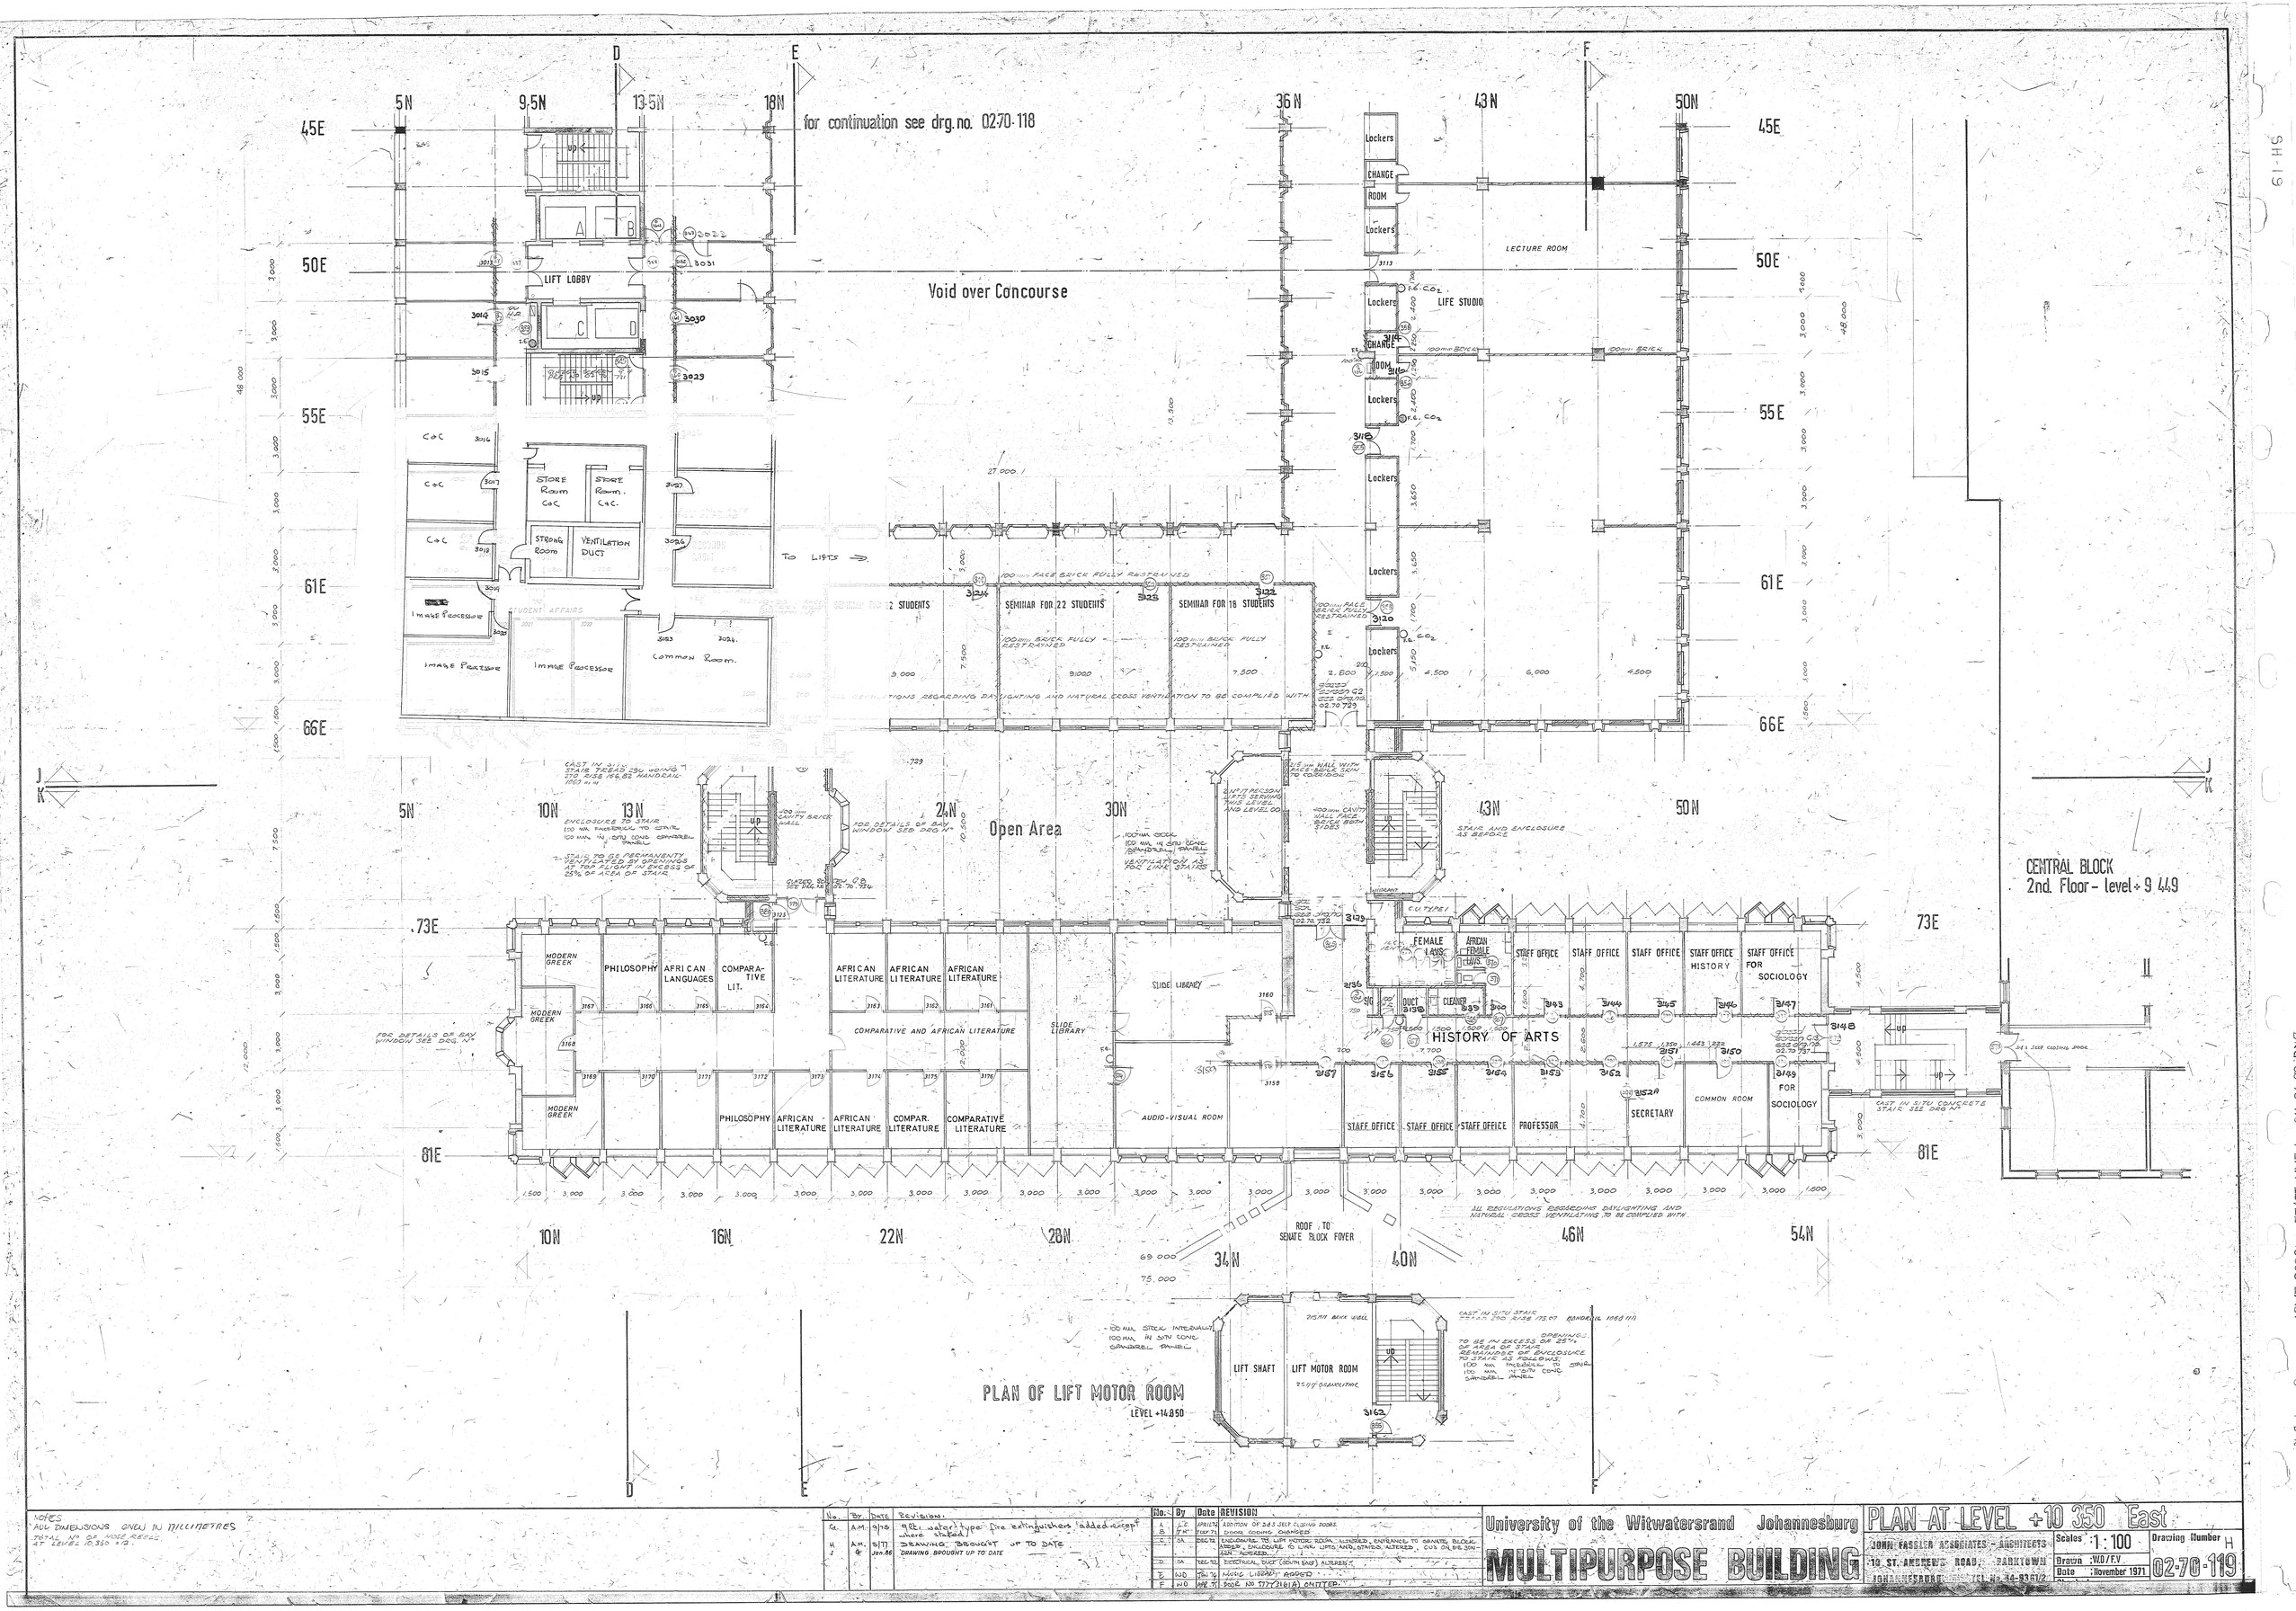

CENTRAL BLOCK
2nd. Floor – level + 9 449

SH-19

DRG. 02-70-119 PLAN LEVEL + 10350 EAST 3RD FLR.

NOTES
ALL DIMENSIONS GIVEN IN MILLIMETRES
TOTAL Nº OF HOSE REELS AT LEVEL 10.350 = 12.

No.	By	DATE	REVISIONS
G	A.M.	9/75	9 Kg. water type fire extinguishers added except where stated
H	A.M.	5/77	DRAWING BROUGHT UP TO DATE
J	"	Jan. 86	DRAWING BROUGHT UP TO DATE

No.	By	Date	REVISION
A	JC	APR 72	ADDITION OF 343 SELF CLOSING DOORS
B	TM	SEP 71	DOOR CODING CHANGES
C	SA	DEC 72	ENCLOSURE TO LIFT MOTOR ROOM ALTERED, ENTRANCE TO SENATE BLOCK FOYER, ENCLOSURE TO LIFT LOBBY AND STAIRS ALTERED, CUT OUT FOR SIN-GEN ADDED
D	SA	DEC 72	MECHANICAL DUCT (DOWN 1ST) ALTERED
E	WD	JAN 74	MUSIC LIBRARY ADDED
F	WD	APR 74	DOOR 330 777-2161(A) OMITTED

University of the Witwatersrand Johannesburg

MULTIPURPOSE BUILDING

PLAN AT LEVEL +10 350 East

JOHN FASSLER ASSOCIATES - ARCHITECTS
19 ST. ANDREWS ROAD PARKTOWN
JOHANNESBURG TEL. NO. 34-8956/2

Scales 1 : 100
Drawn WD/FV
Date November 1971

Drawing Number H
02-70-119