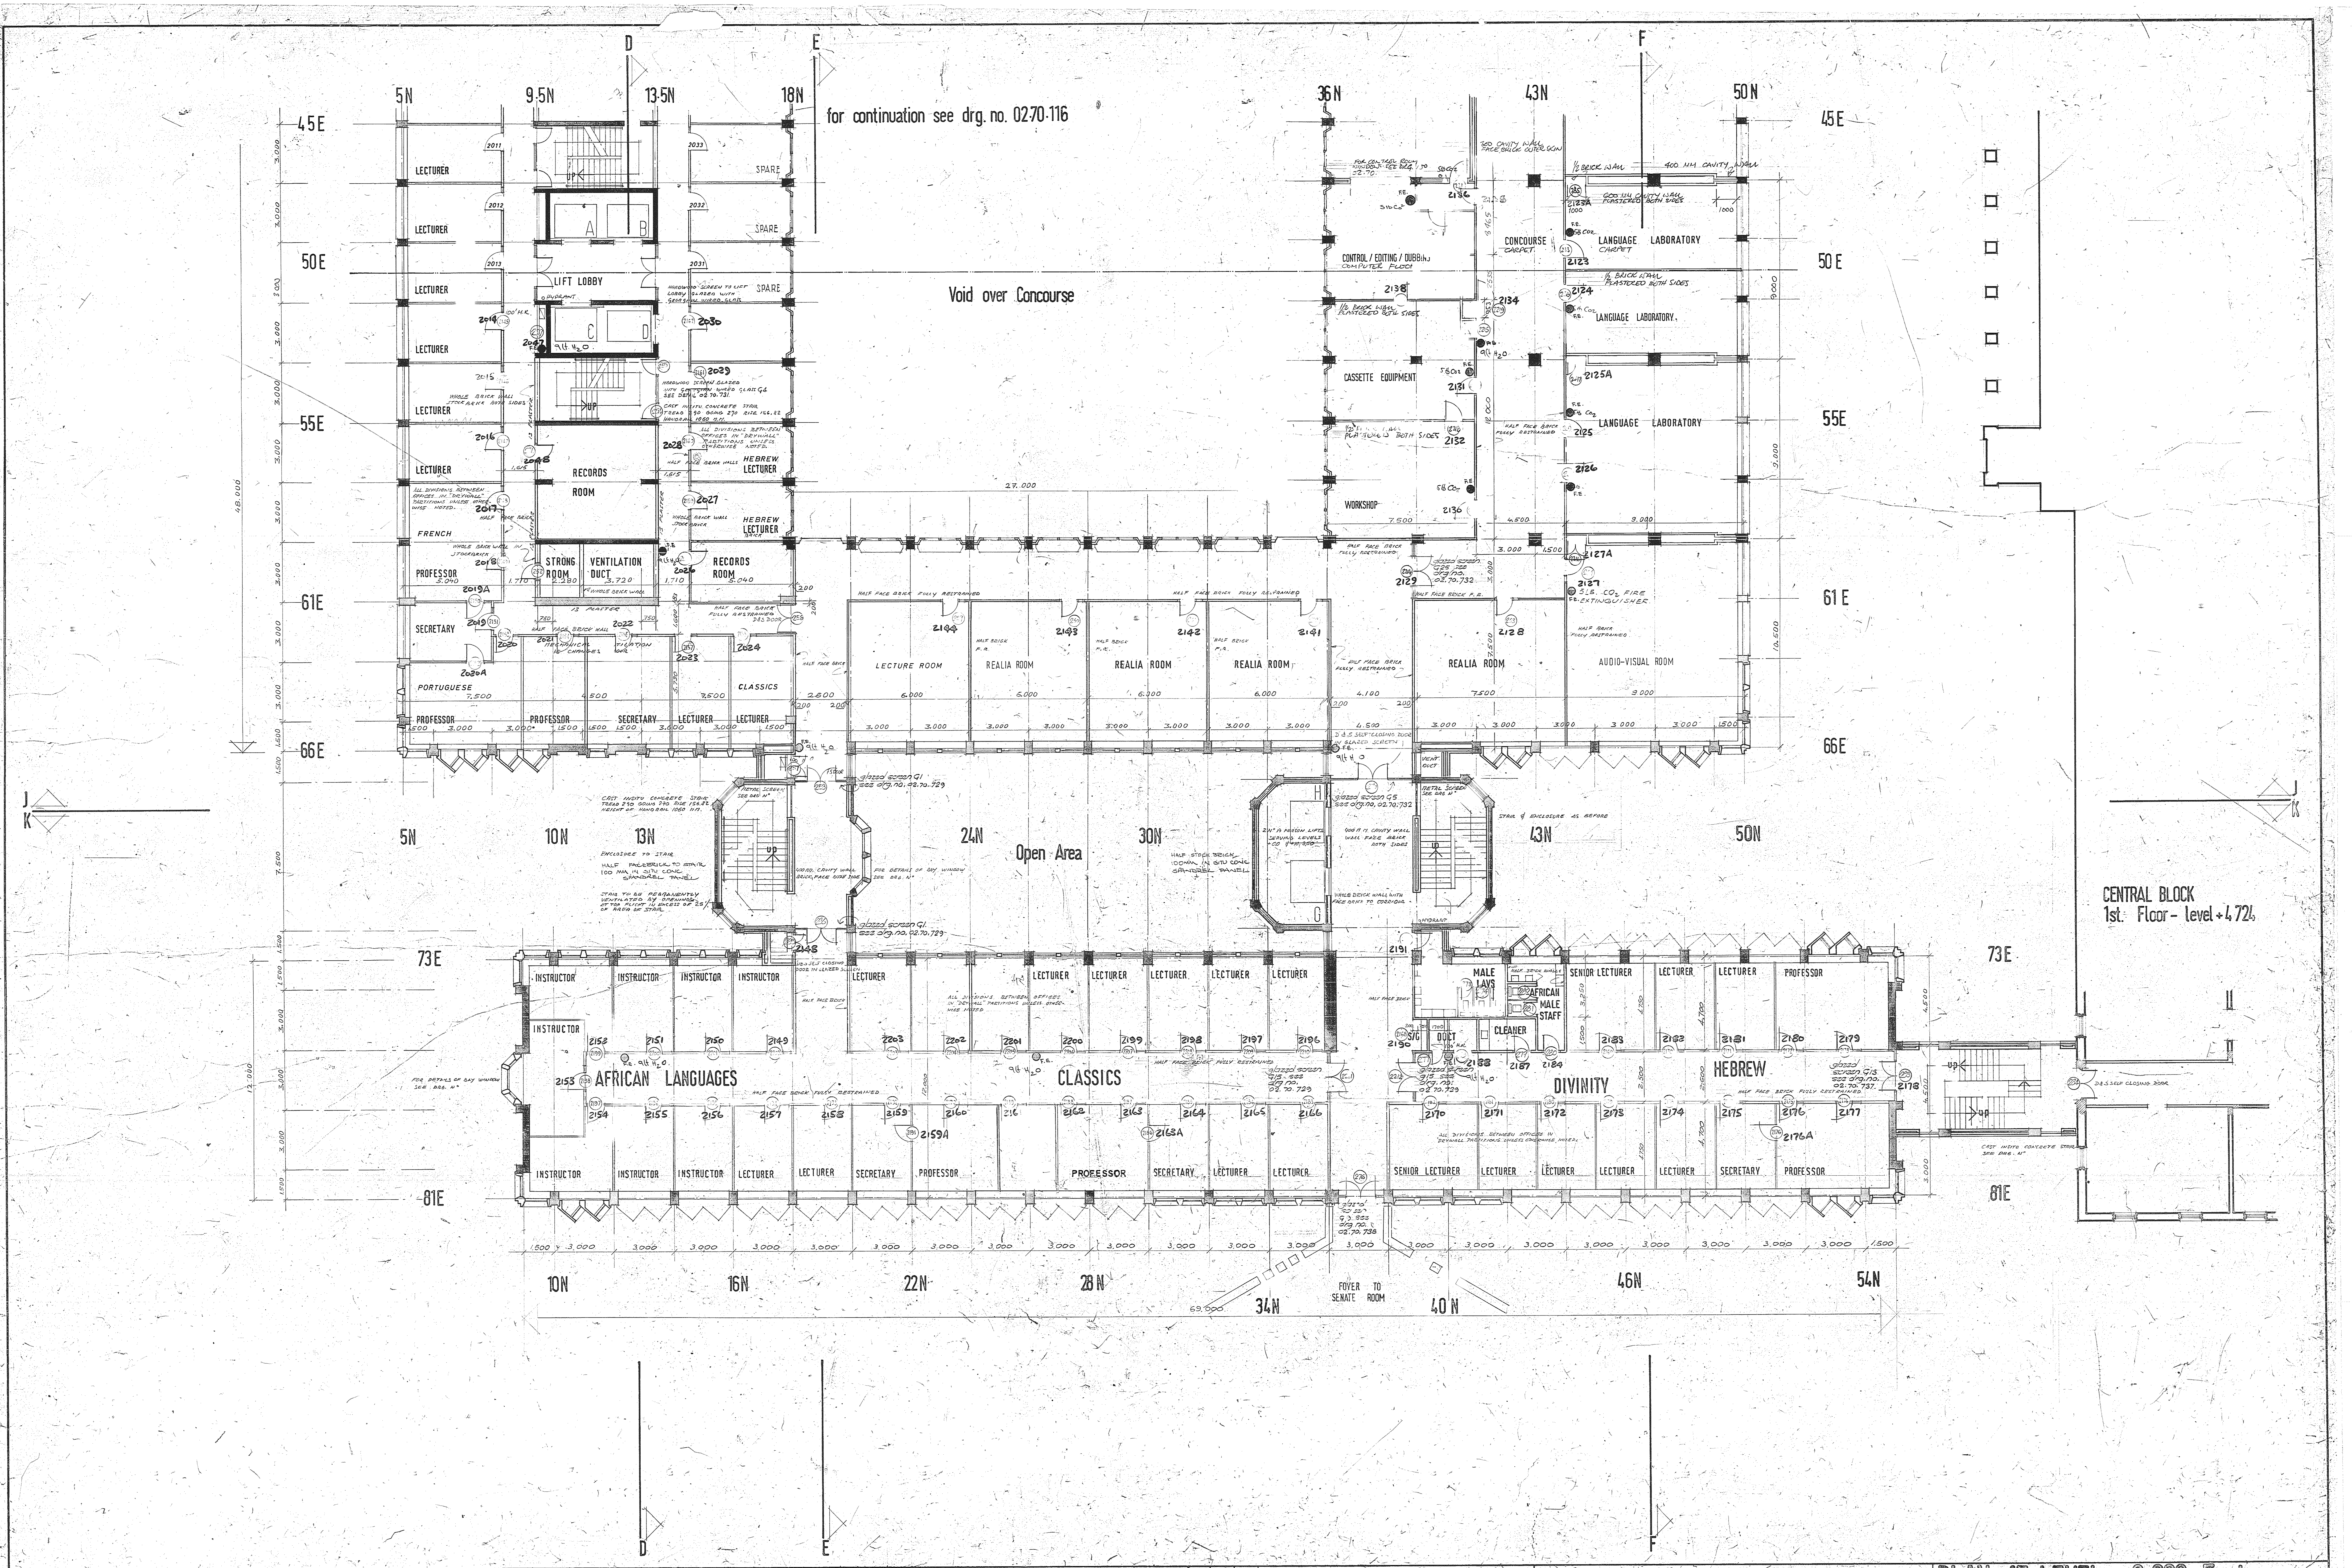

NOTES
ALL DIMENSIONS GIVEN IN MILLIMETRES
TOTAL N° OF HOSE REELS AT LEVEL 6,900 = 72

No	By	DATE	REVISION
9.	N.D	DEC 73	LAYOUT OF LANGUAGE LABS & TECHNICAL AREAS ALTERED TOWER CORE PLASTERED
H.	A.M.	SEP 75	9 lt water type fire extinguishers added - F.E. except where indikated.
I	A.M.	MAY 77	DRAWING BROUGHT UP TO DATE.

No.	By	Date	REVISION
A	L.C.	APRIL 72	ADDITIONS OF D&S SELF CLOSING DOORS
B	T.K.	JULY 72	DOOR CODINGS CHANGED
C	L.C.	JULY 72	ALTERATIONS TO STUDIO AREA LAYOUT
D	SA	DEC 72	CU'S ON 81E 30N TO 42N ALTERED, ENTRANCE TO SENATE BLOCK ADDED, ENCLOSURES TO LINK LIFTS & STAIRS ALTERED.
E	SA	DEC 72	SOUTH-EAST ELECTRICAL DUCT ALTERED.
F	C.K.P.	AUG 73	OFFICE LAYOUT ADDED. DOORS TO OFFICES ADDED & NUMBERED.

University of the Witwatersrand Johannesburg

MULTIPURPOSE BUILDING

PLAN AT LEVEL +6 900 East

JOHN FASSLER ASSOCIATES - ARCHITECTS
16 ST. ANDREWS ROAD, PARKTOWN
JOHANNESBURG TEL. No. 44-[illegible]

Scales : 1 : 100
Drawn : W.O / F.V
Date : November 1971
Checked :

Drawing Number I
02-70-117

SH-17

DRG. 02-70-117 PLAN-LEVEL +6900 EAST 2nd FLR